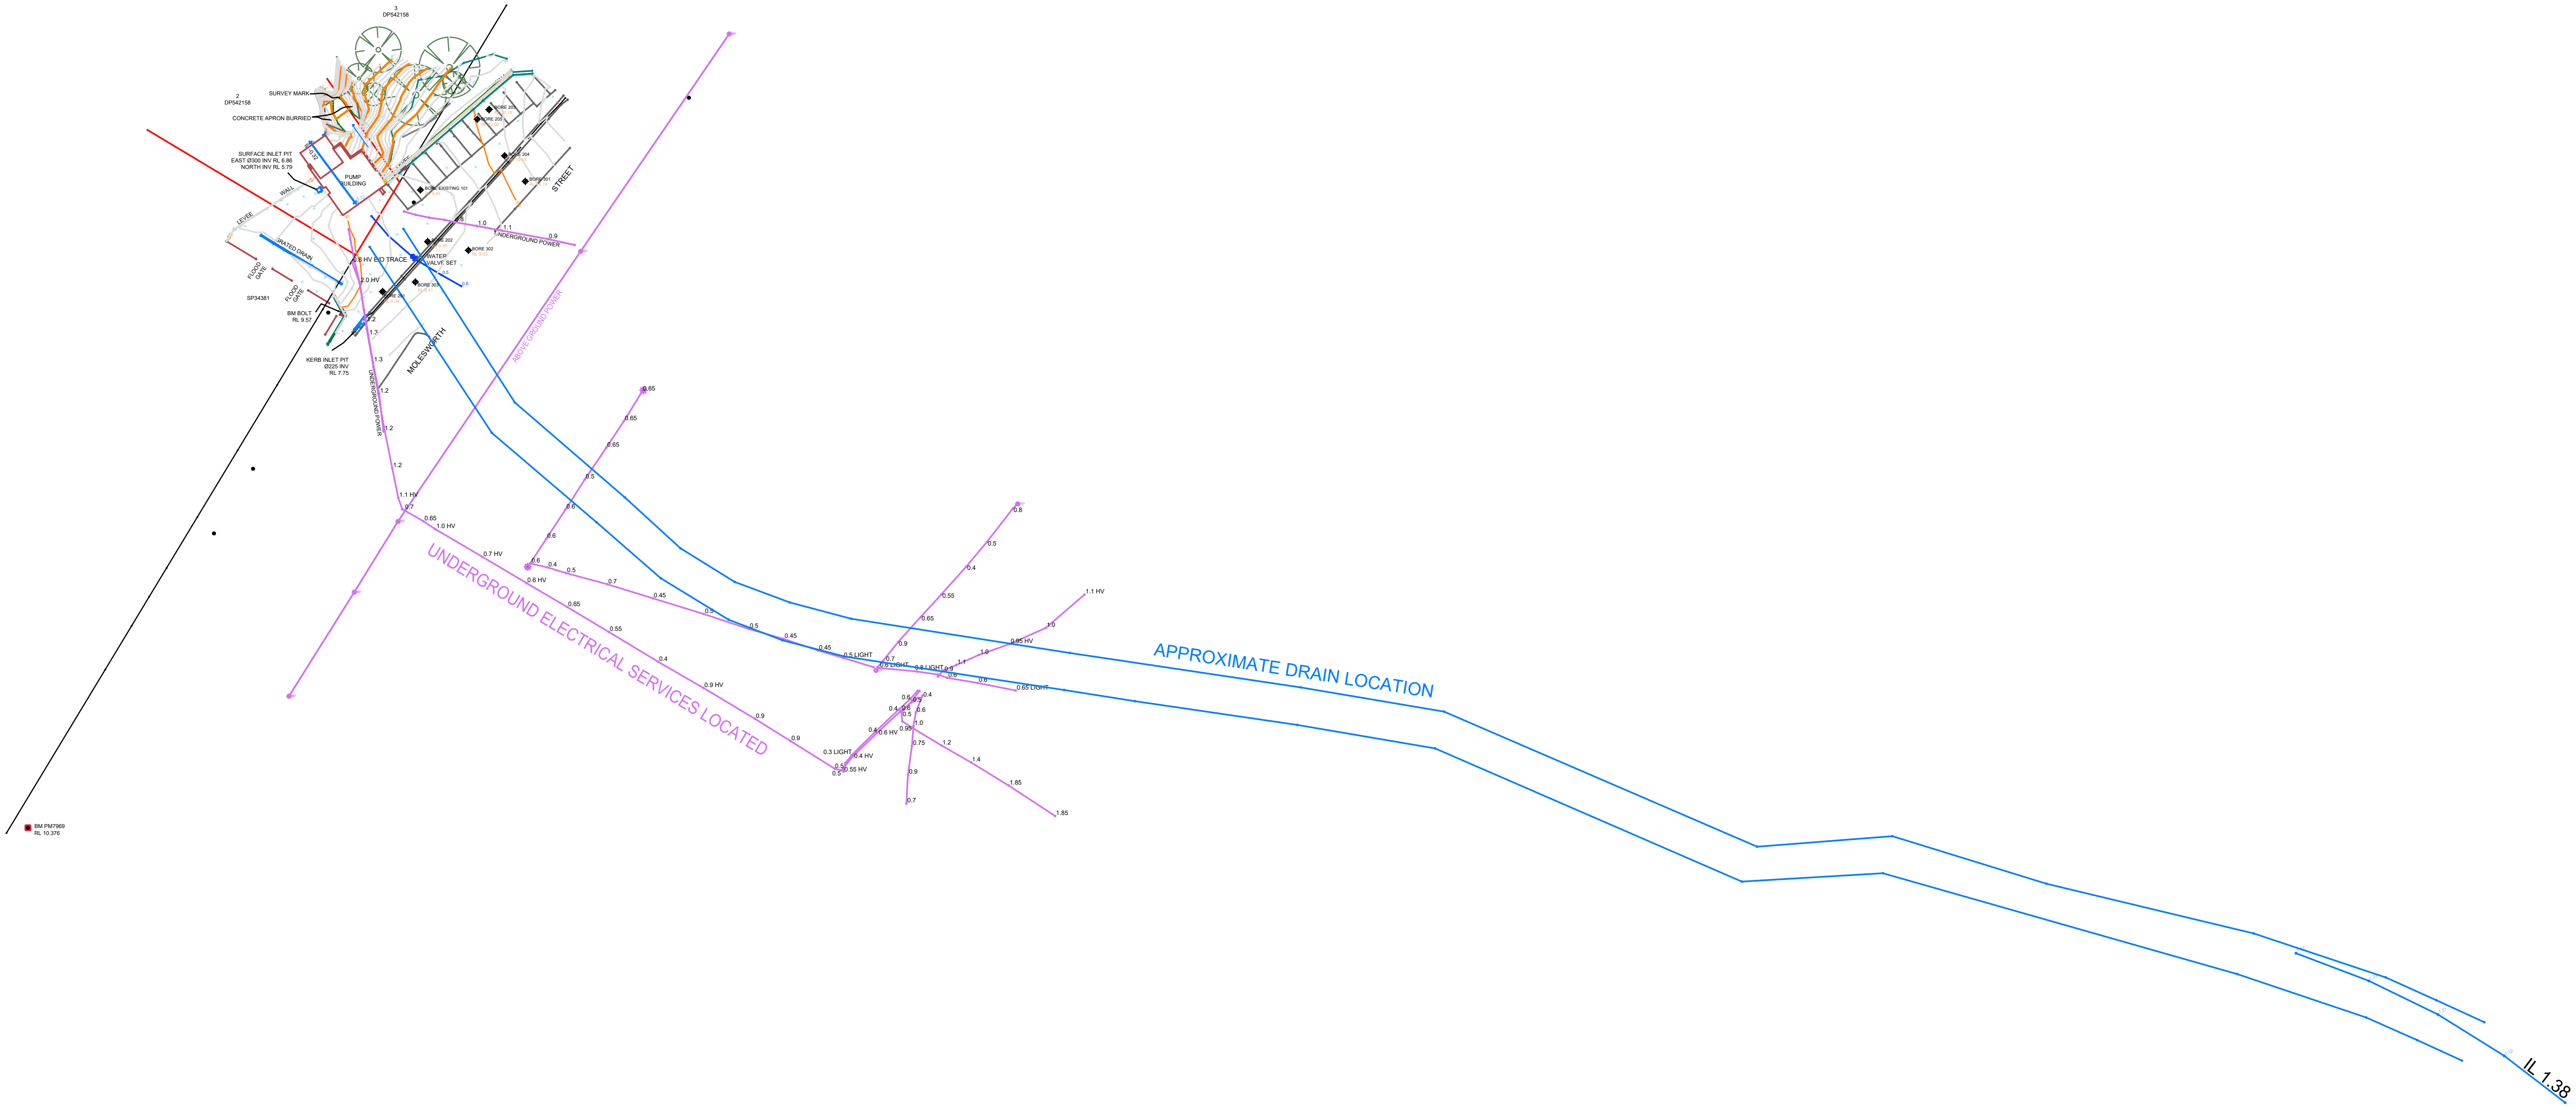
3
DP542158
2
DP542158
SURVEY MARK
CONCRETE APRON BURRIED
SURFACE INLET PIT
EAST Ø300 INV RL 6.86
NORTH INV RL 5.79
PUMP
BUILDING
WALL
LEVEE
GRATED DRAIN
FLOOD
GATE
FLOOD
GATE
SP34381
BM BOLT
RL 9.57
KERB INLET PIT
Ø225 INV
RL 7.75
BORE 203
RL 10.10
BORE 205
RL 10.00
BORE 204
RL 10.18
BORE 301
RL 10.14
BORE EXISTING 101
RL 9.45
BORE 202
RL 9.38
BORE 302
RL 9.63
BORE 303
RL 9.41
BORE 201
RL 9.34
STREET
MOLESWORTH
0.8 HV E/O TRACE
WATER
VALVE SET
2.0 HV
UNDERGROUND POWER
UNDERGROUND POWER
ABOVE GROUND POWER
UNDERGROUND ELECTRICAL SERVICES LOCATED
APPROXIMATE DRAIN LOCATION
IL 1.38
BM PM7969
RL 10.376